

NHÀ Ở 2 TẦNG 17 × 7 M

HỒ SƠ THIẾT KẾ PHƯƠNG ÁN KIẾN TRÚC · KT-01

Bảo ALONE · CREATIVE STUDIO · GAME STUDIO


0932 705 063

KÍCH THƯỚC NHÀ	SỐ TẦNG	DIỆN TÍCH SÀN	PHÒNG NGỦ	CHIỀU CAO TẦNG	ĐỈNH MÁI
17 × 7 m	2 tầng + mái bằng	184 m²	4 phòng	3.300 mm	+7.400

DANH MỤC BẢN VẼ

KT-00	BÌA · DANH MỤC BẢN VẼ	–
KT-01	MẶT BẰNG TẦNG 1	1:75
KT-02	MẶT BẰNG TẦNG 2	1:75
KT-03	MẶT BẰNG MÁI · TỔNG THỂ	1:75 · 1:250
KT-04	MẶT ĐỨNG CHÍNH · MẶT ĐỨNG SAU	1:100
KT-05	MẶT ĐỨNG BÊN TRÁI · BÊN PHẢI	1:75
KT-06	MẶT CẮT A-A · B-B	1:100

Mô hình 3D tương tác: auudii-house.netlify.app · Ngày phát hành 22/10/2026 · Bản vẽ phương án, kích thước cần xác nhận lại trước khi thi công.

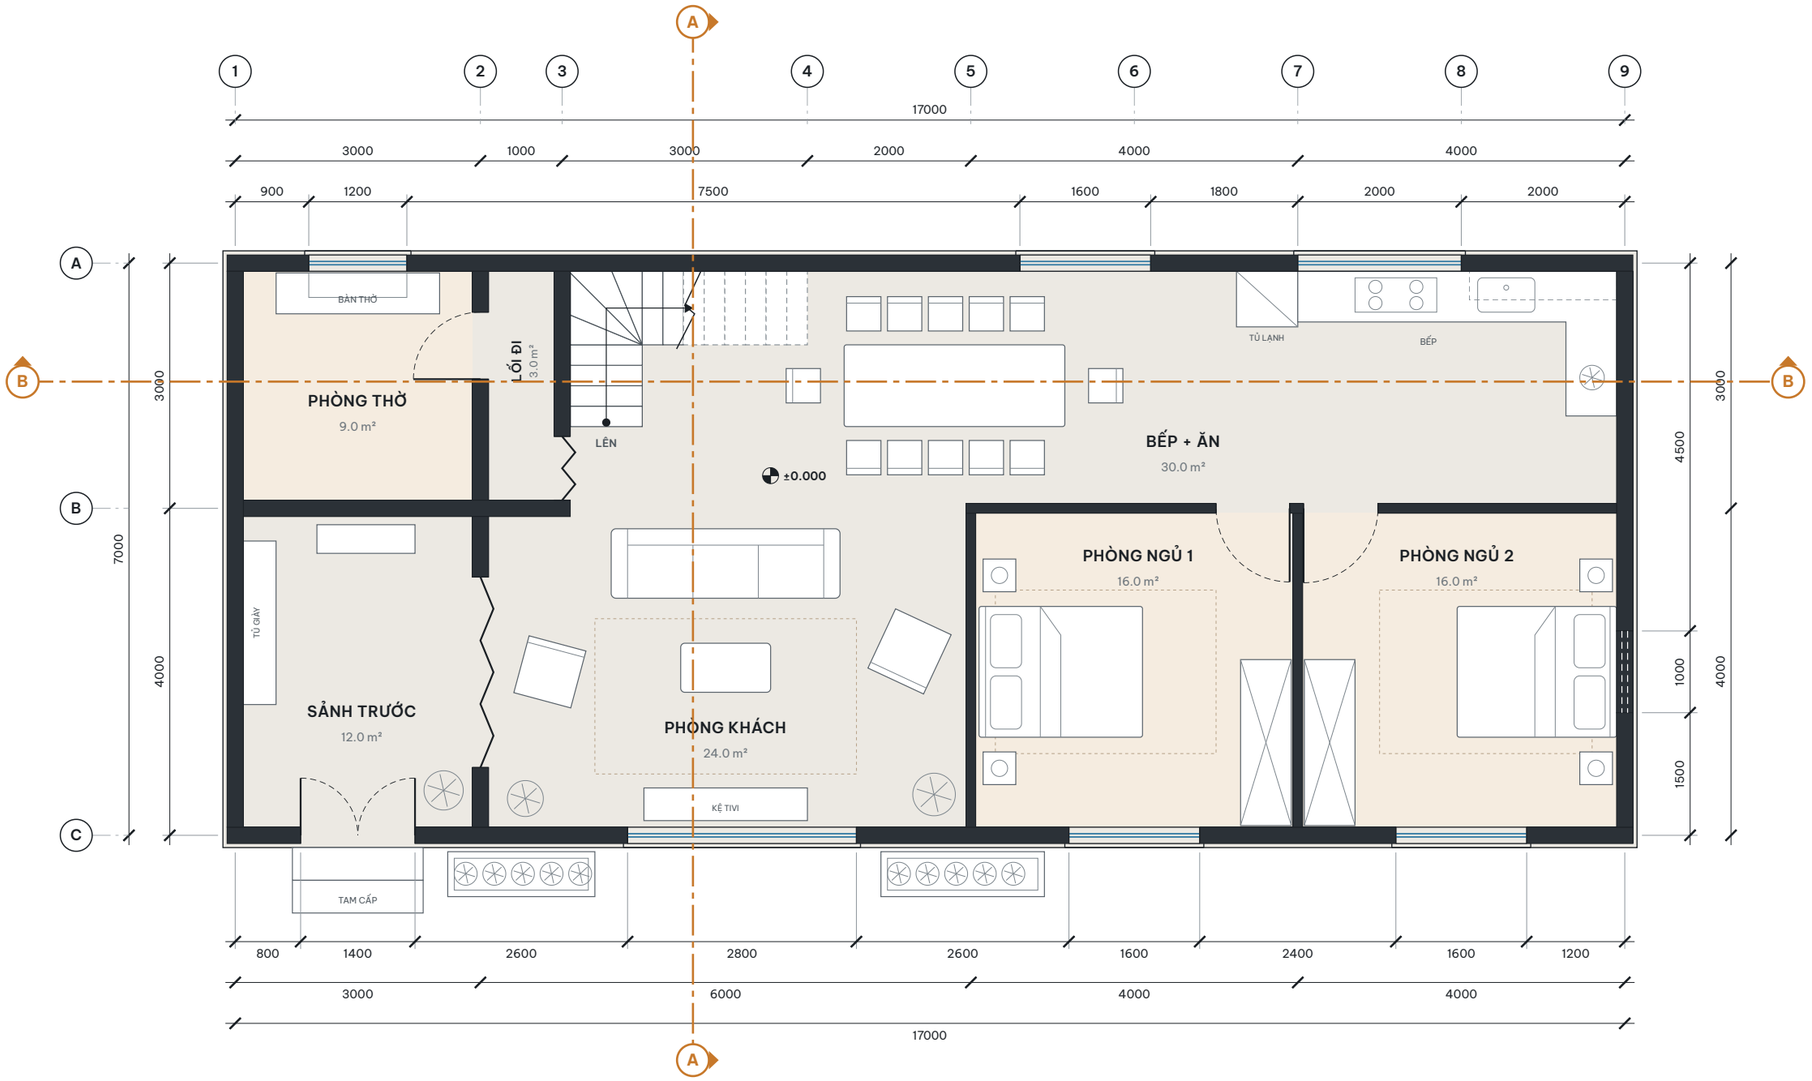

MẶT BẰNG TẦNG 1

TỈ LỆ 1:75

Bảo ALONE

CREATIVE STUDIO · GAME STUDIO

THIẾT KẾ · LIÊN HỆ

0932 705 063

GHI CHÚ

1. Kích thước ghi theo trục tường, đơn vị mm; cao độ đơn vị m.
2. Cao độ ±0.000 lấy tại mặt sàn hoàn thiện tầng 1; sân −0.450.
3. Tường bao 200, tường ngăn 100–200.
4. Cầu thang chữ L: 4 bậc + 4 bậc xoay + 8 bậc, 17 cổ bậc ≈ 194, mặt bậc 250.
5. Bản vẽ phương án, dựng lại từ phác thảo tay và mô hình 3D; vị trí cửa, nội thất và kết cấu cần chủ nhà xác nhận trước khi triển khai kỹ thuật.

KÝ HIỆU

- Tường xây (cắt)
- Tường ốp gỗ (cắt)
- Kính cửa sổ / lan can
- Cửa sổ cao (trên mặt cắt)
- Mép mái / kết cấu phía trên
- Sàn gỗ
- Sàn gỗ ngoài trời
- Sàn đá / gạch
- Vị trí mặt cắt

CÔNG TRÌNH
NHÀ Ở 2 TẦNG 17 × 7 M

MÃ PHƯƠNG ÁN
KT-01 · nhà ở 2 tầng · 184 m² sàn


GIAI ĐOẠN
THIẾT KẾ PHƯƠNG ÁN

NGÀY
22/10/2026

TỈ LỆ
1:75 (khổ A3)

TÊN BẢN VẼ
MẶT BẰNG TẦNG 1

SỐ BẢN VẼ
KT-01

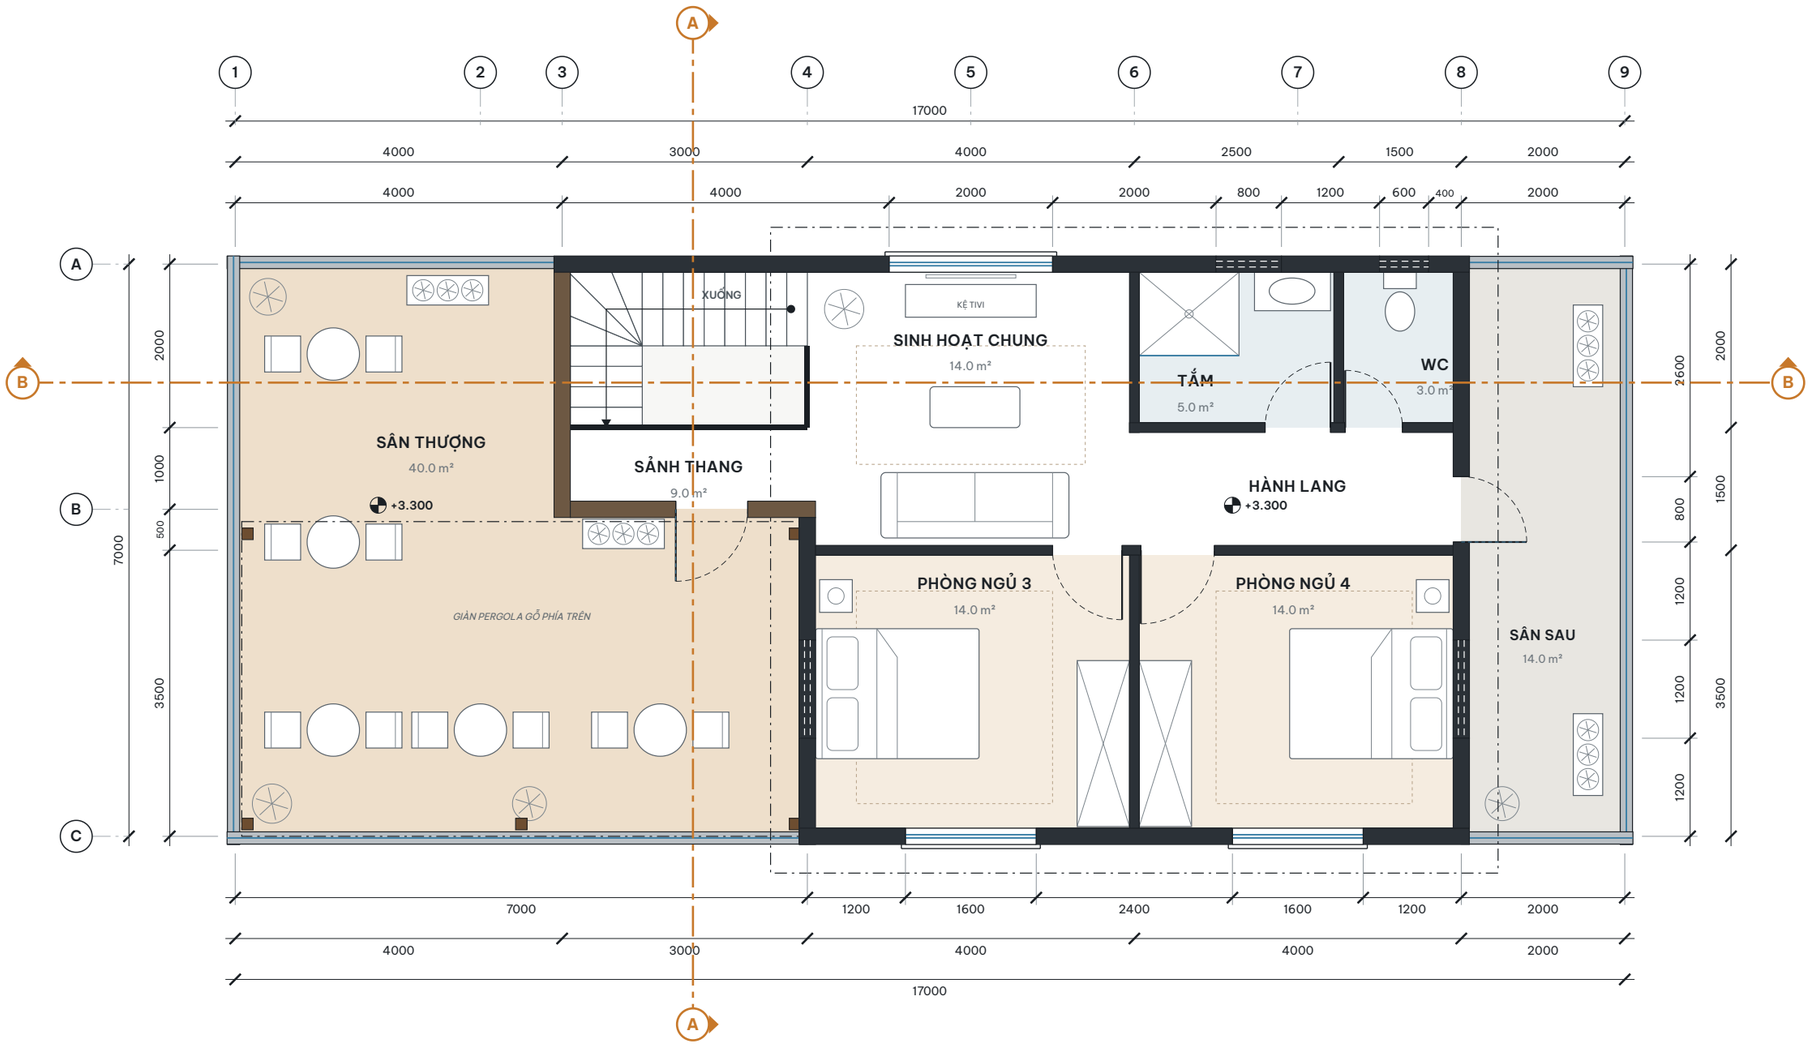

MẶT BẰNG TẦNG 2

TỈ LỆ 1:75

Bảo ALONE

CREATIVE STUDIO · GAME STUDIO

THIẾT KẾ · LIÊN HỆ

0932 705 063

GHI CHÚ

1. Kích thước ghi theo trục tường, đơn vị mm; cao độ đơn vị m.
2. Cao độ ±0.000 lấy tại mặt sàn hoàn thiện tầng 1; sân −0.450.
3. Tường bao 200, tường ngăn 100–200.
4. Cầu thang chữ L: 4 bậc + 4 bậc xoay + 8 bậc, 17 cổ bậc ≈ 194, mặt bậc 250.
5. Bản vẽ phương án, dựng lại từ phác thảo tay và mô hình 3D; vị trí cửa, nội thất và kết cấu cần chủ nhà xác nhận trước khi triển khai kỹ thuật.

KÝ HIỆU

- Tường xây (cắt)
- Tường ốp gỗ (cắt)
- Kính cửa sổ / lan can
- Cửa sổ cao (trên mặt cắt)
- Mép mái / kết cấu phía trên
- Sàn gỗ
- Sàn gỗ ngoài trời
- Sàn đá / gạch
- Vị trí mặt cắt

CÔNG TRÌNH
NHÀ Ở 2 TẦNG 17 × 7 M

MÃ PHƯƠNG ÁN
KT-01 · nhà ở 2 tầng · 184 m² sàn


GIAI ĐOẠN
THIẾT KẾ PHƯƠNG ÁN

NGÀY
22/10/2026

TỈ LỆ
1:75 (khổ A3)


TÊN BẢN VẼ
MẶT BẰNG TẦNG 2

SỐ BẢN VẼ
KT-02

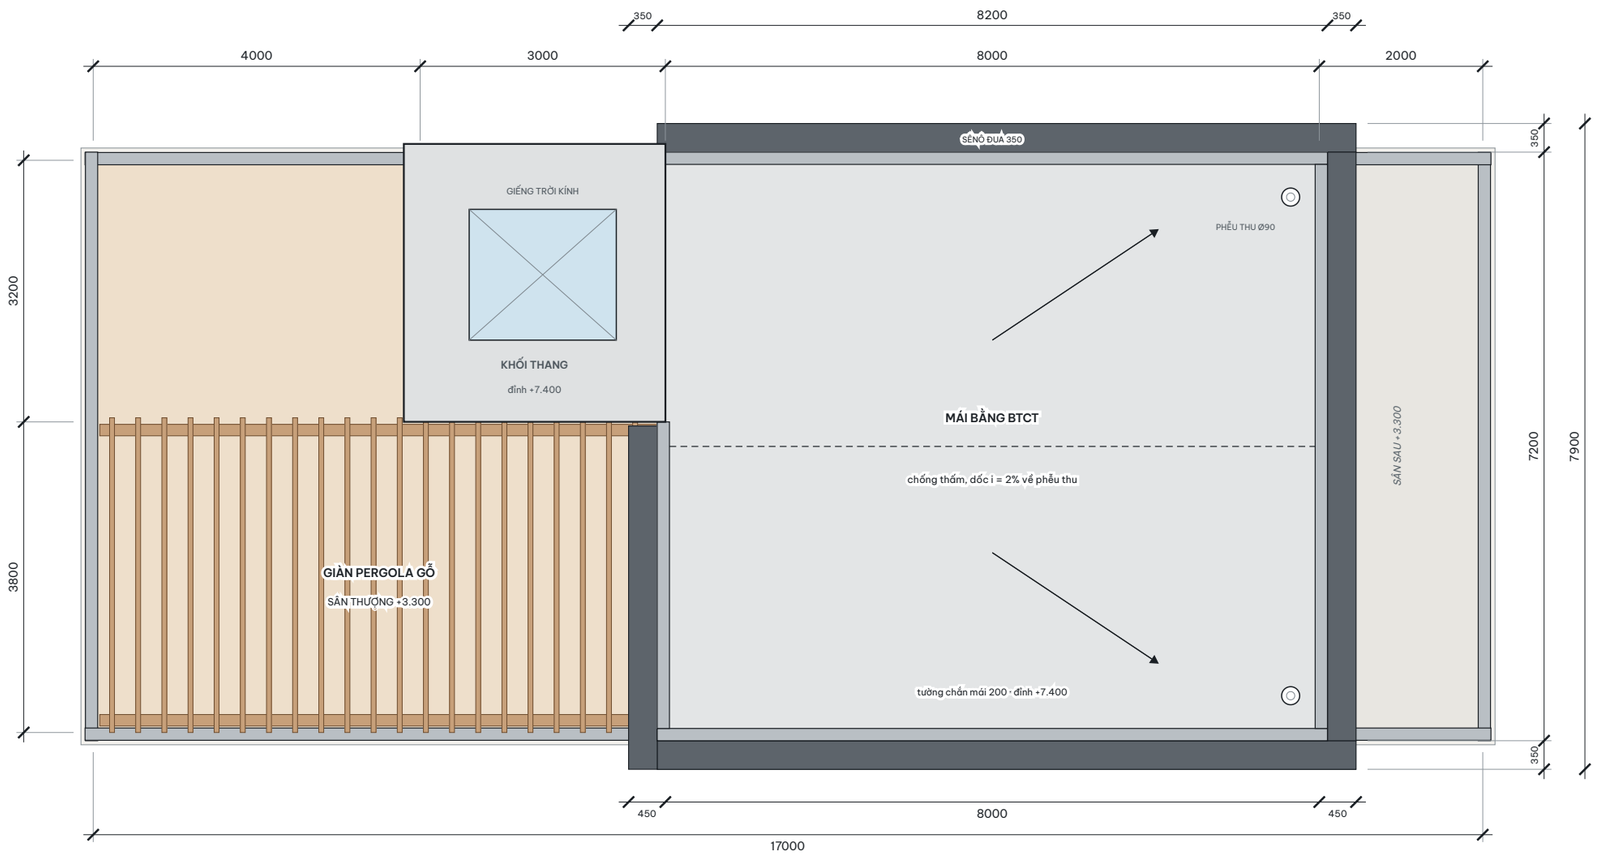

MẶT BẰNG MÁI

TỈ LỆ 1:75

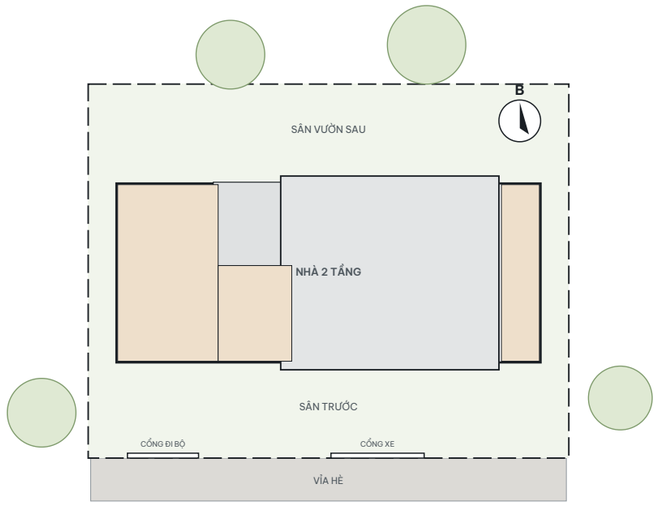

MẶT BẰNG TỔNG THỂ

TỈ LỆ 1:250 · hướng Bắc giả định

Khu đất 19.6 × 15 m, nhà lùi 3.7 m so với ranh trước.
Cổng đi bộ 2.9 m, cổng xe 3.8 m; tường rào đá + bờ giậu.
Sân sau 4 m, hàng rào thép thấp phía sau.

Bảo ALONE
CREATIVE STUDIO · GAME STUDIO
THIẾT KẾ · LIÊN HỆ
0932 705 063

GHI CHÚ

1. Kích thước ghi theo trục tường, đơn vị mm; cao độ đơn vị m.
2. Cao độ ±0.000 lấy tại mặt sàn hoàn thiện tầng 1; sân −0.450.
3. Tường bao 200, tường ngăn 100–200.
4. Cầu thang chữ L: 4 bậc + 4 bậc xoay + 8 bậc, 17 cổ bậc ≈ 194, mặt bậc 250.
5. Bản vẽ phương án, dựng lại từ phác thảo tay và mô hình 3D; vị trí cửa, nội thất và kết cấu cần chủ nhà xác nhận trước khi triển khai kỹ thuật.

CÔNG TRÌNH
NHÀ Ở 2 TẦNG 17 × 7 M

MÃ PHƯƠNG ÁN
KT-01 · nhà ở 2 tầng · 184 m² sàn


GIAI ĐOẠN
THIẾT KẾ PHƯƠNG ÁN

NGÀY
22/10/2026

TỈ LỆ
1:75 · 1:250 (khổ A3)


TÊN BẢN VẼ
MẶT BẰNG MÁI · TỔNG THỂ

SỐ BẢN VẼ
KT-03

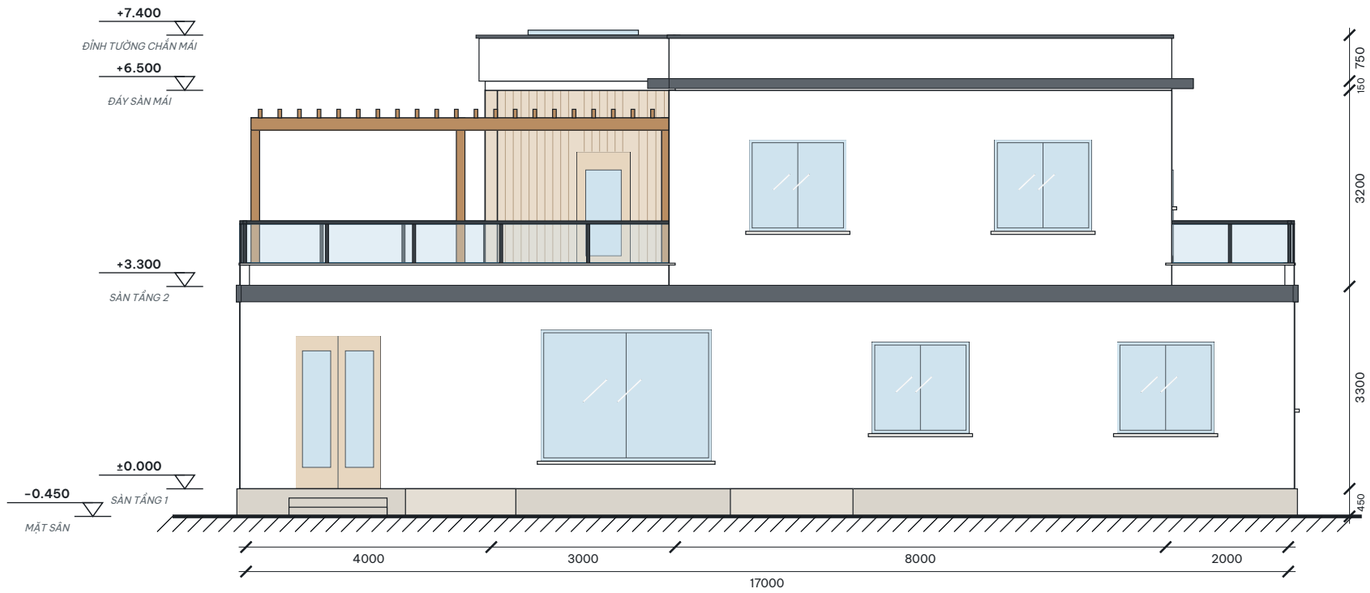

MẶT ĐỨNG CHÍNH (TRỤC 1 → 9)

TỈ LỆ 1:100

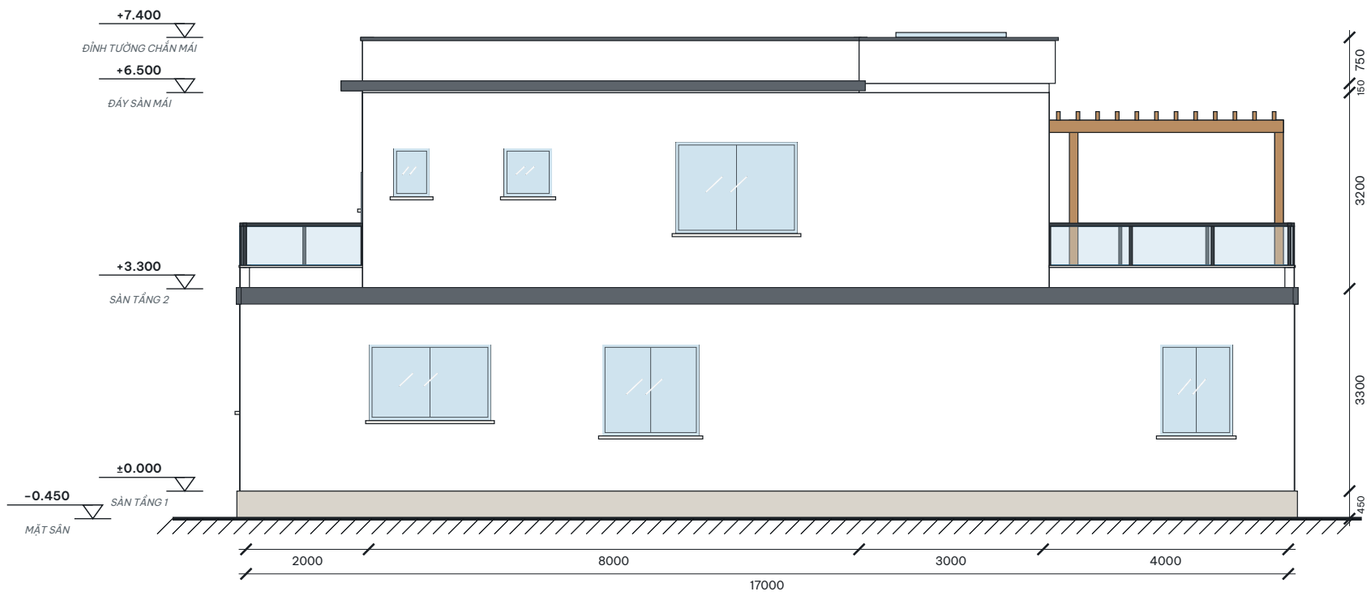

MẶT ĐỨNG SAU (TRỤC 9 → 1)

TỈ LỆ 1:100

Bảo ALONE
CREATIVE STUDIO · GAME STUDIO
THIẾT KẾ · LIÊN HỆ
0932 705 063

GHI CHÚ

1. Kích thước ghi theo trục tường, đơn vị mm; cao độ đơn vị m.
2. Cao độ ±0.000 lấy tại mặt sàn hoàn thiện tầng 1; sân −0.450.
3. Tường bao 200, tường ngăn 100–200.
4. Cầu thang chữ L: 4 bậc + 4 bậc xoay + 8 bậc, 17 cổ bậc ≈ 194, mặt bậc 250.
5. Bản vẽ phương án, dựng lại từ phác thảo tay và mô hình 3D; vị trí cửa, nội thất và kết cấu cần chủ nhà xác nhận trước khi triển khai kỹ thuật.

VẬT LIỆU

- Sơn nước trắng
- Ốp gỗ óc chó (ô thang)
- Kính khung nhôm đen
- Viền sàn, sênô sơn ghi
- Gỗ pergola
- Đá ốp chân tường

CÔNG TRÌNH
NHÀ Ở 2 TẦNG 17 × 7 M

MÃ PHƯƠNG ÁN
KT-01 · nhà ở 2 tầng · 184 m² sàn


GIAI ĐOẠN
THIẾT KẾ PHƯƠNG ÁN

NGÀY
22/10/2026

TỈ LỆ
1:100 (khổ A3)


TÊN BẢN VẼ
MẶT ĐỨNG CHÍNH · MẶT ĐỨNG SAU

SỐ BẢN VẼ
KT-04

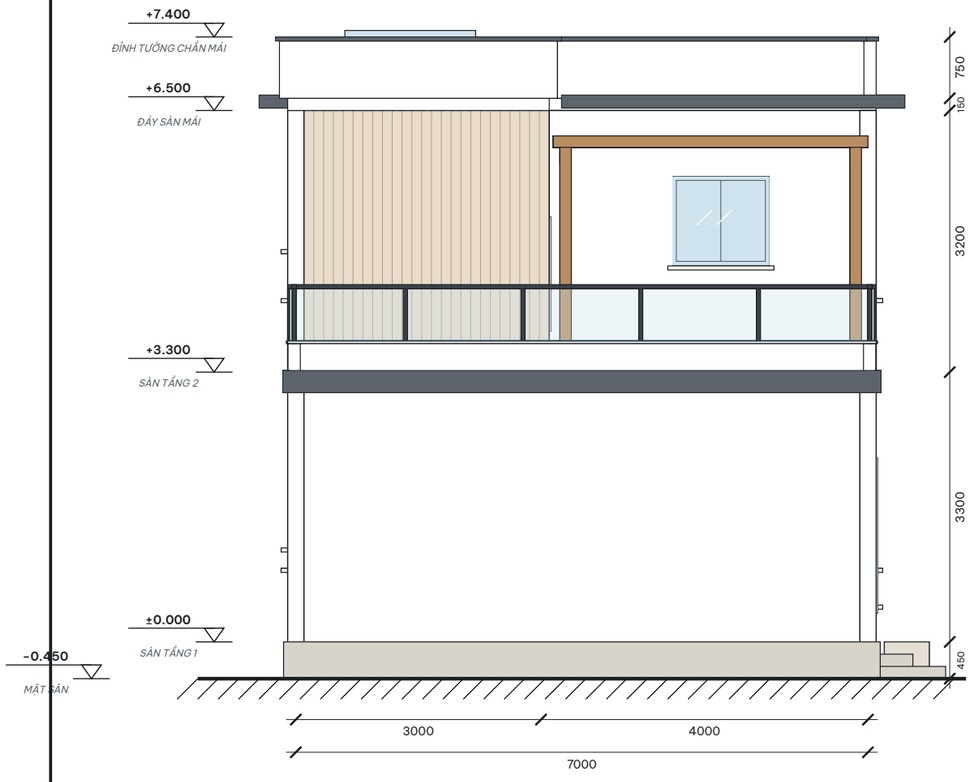

MẶT ĐỨNG BÊN TRÁI (TRỤC A → C)

TỈ LỆ 1:75

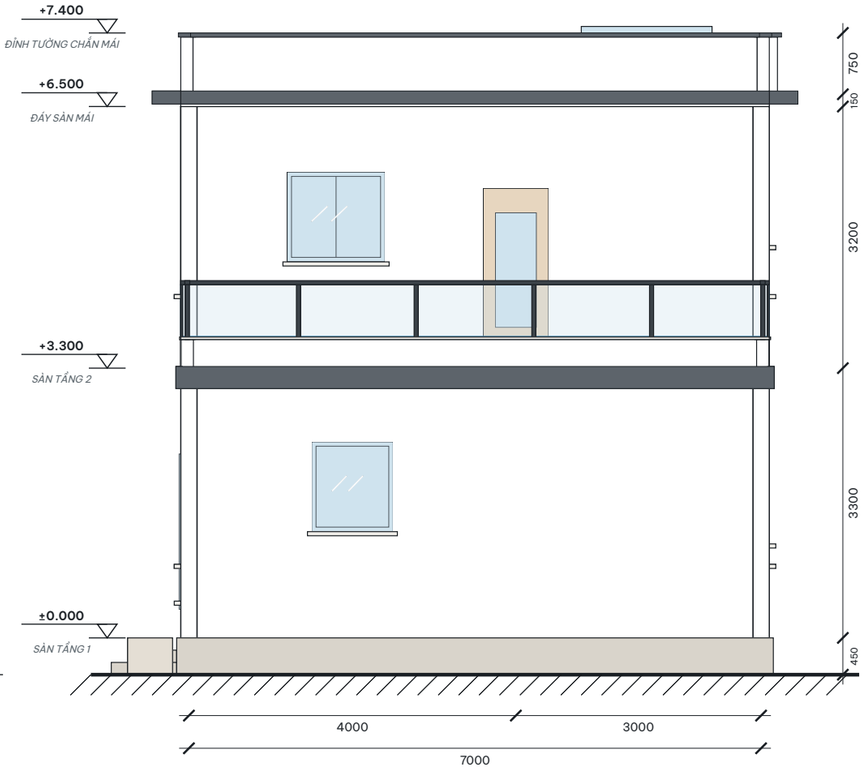

MẶT ĐỨNG BÊN PHẢI (TRỤC C → A)

TỈ LỆ 1:75

Bảo ALONE

CREATIVE STUDIO · GAME STUDIO

THIẾT KẾ · LIÊN HỆ

0932 705 063

GHI CHÚ

1. Kích thước ghi theo trục tường, đơn vị mm; cao độ đơn vị m.
2. Cao độ ±0.000 lấy tại mặt sàn hoàn thiện tầng 1; sân −0.450.
3. Tường bao 200, tường ngăn 100–200.
4. Cầu thang chữ L: 4 bậc + 4 bậc xoay + 8 bậc, 17 cổ bậc ≈ 194, mặt bậc 250.
5. Bản vẽ phương án, dựng lại từ phác thảo tay và mô hình 3D; vị trí cửa, nội thất và kết cấu cần chủ nhà xác nhận trước khi triển khai kỹ thuật.

VẬT LIỆU

- Sơn nước trắng
- Ốp gỗ óc chó (ô thang)
- Kính khung nhôm đen
- Viền sàn, sênô sơn ghi
- Gỗ pergola

CÔNG TRÌNH
NHÀ Ở 2 TẦNG 17 × 7 M

MÃ PHƯƠNG ÁN
KT-01 · nhà ở 2 tầng · 184 m² sàn


GIAI ĐOẠN
THIẾT KẾ PHƯƠNG ÁN

NGÀY
22/10/2026

TỈ LỆ
1:75 (khổ A3)


TÊN BẢN VẼ
MẶT ĐỨNG BÊN TRÁI · BÊN PHẢI

SỐ BẢN VẼ
KT-05

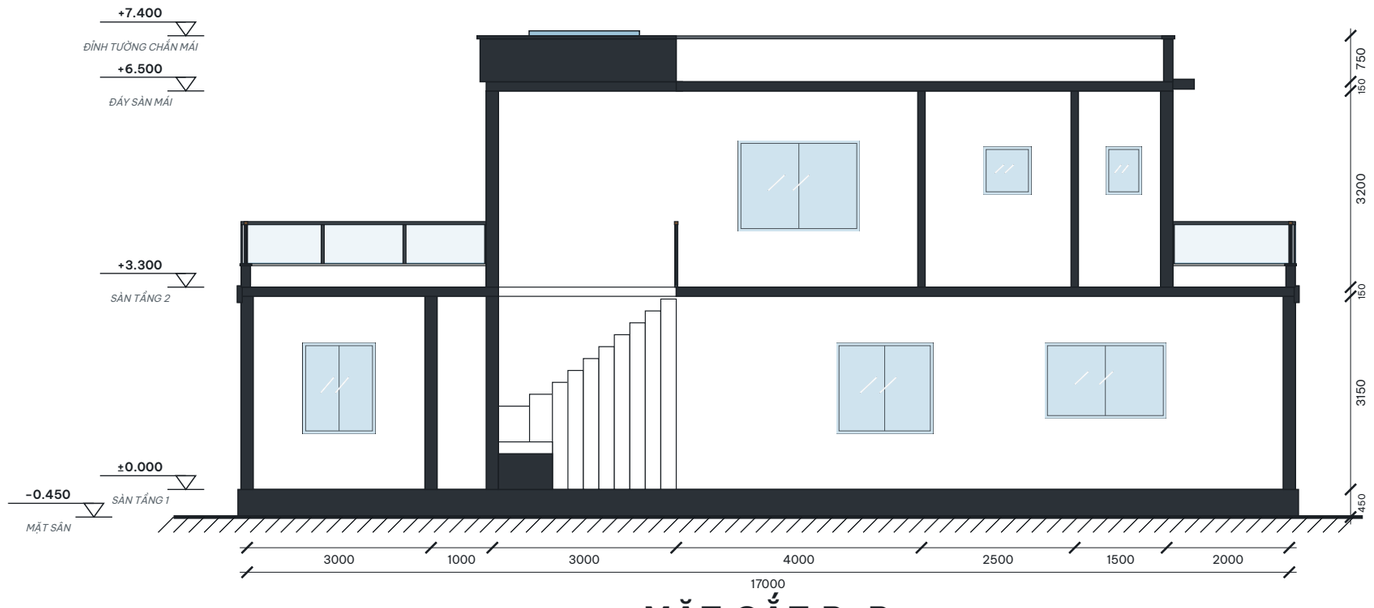

MẶT CẮT B-B

TỈ LỆ 1:100

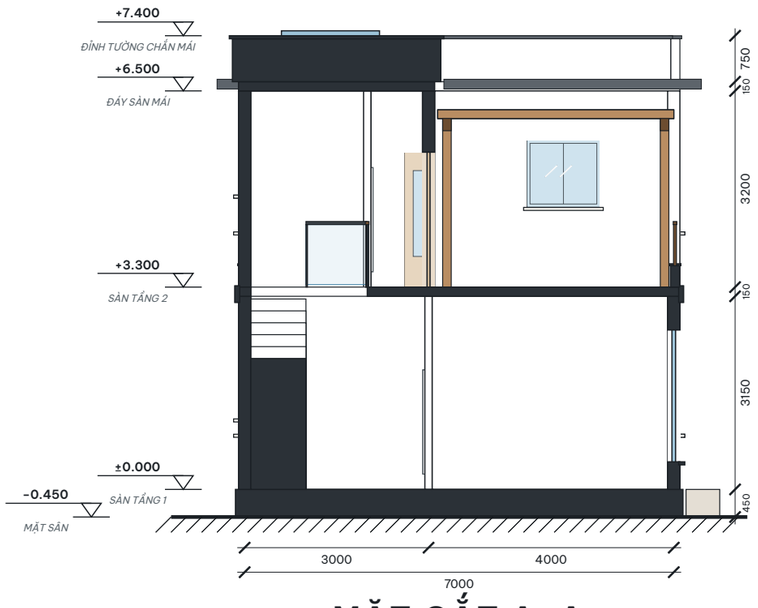

MẶT CẮT A-A

TỈ LỆ 1:100

Bảo ALONE
CREATIVE STUDIO · GAME STUDIO
THIẾT KẾ · LIÊN HỆ
0932 705 063

GHI CHÚ

1. Kích thước ghi theo trục tường, đơn vị mm; cao độ đơn vị m.
2. Cao độ ±0.000 lấy tại mặt sàn hoàn thiện tầng 1; sân -0.450.
3. Tường bao 200, tường ngăn 100–200.
4. Cầu thang chữ L: 4 bậc + 4 bậc xoay + 8 bậc, 17 cổ bậc ≈ 194, mặt bậc 250.
5. Bản vẽ phương án, dựng lại từ phác thảo tay và mô hình 3D; vị trí cửa, nội thất và kết cấu cần chủ nhà xác nhận trước khi triển khai kỹ thuật.

KÝ HIỆU

- Kết cấu / tường bị cắt
- Kính bị cắt
- Phần nhìn thấy phía sau

CÔNG TRÌNH
NHÀ Ở 2 TẦNG 17 × 7 M

MÃ PHƯƠNG ÁN
KT-01 · nhà ở 2 tầng · 184 m² sàn

GIAI ĐOẠN
THIẾT KẾ PHƯƠNG ÁN

NGÀY
22/10/2026

TỈ LỆ
1:100 (khổ A3)

TÊN BẢN VẼ
MẶT CẮT A-A · B-B

SỐ BẢN VẼ
KT-06